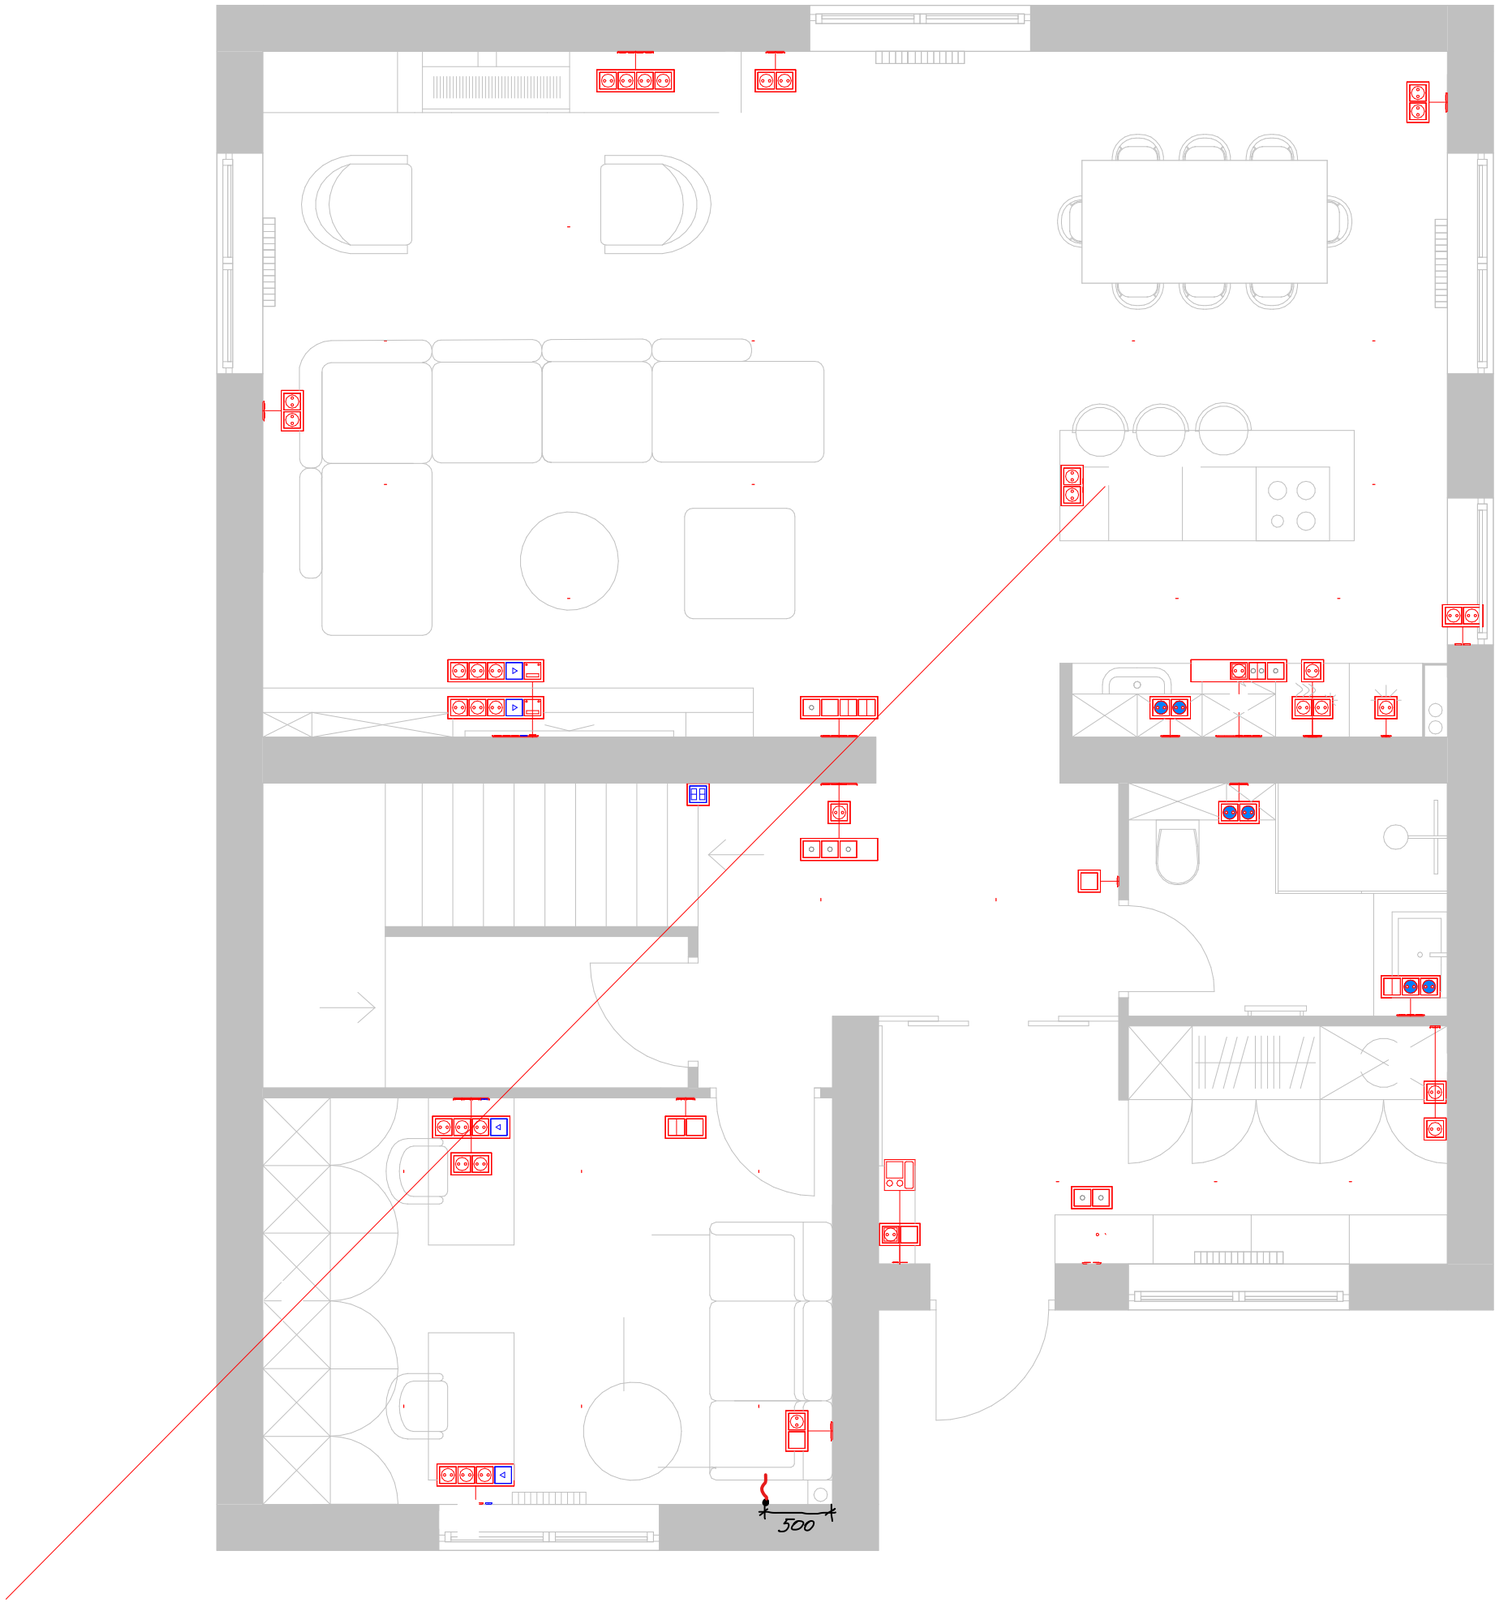
500

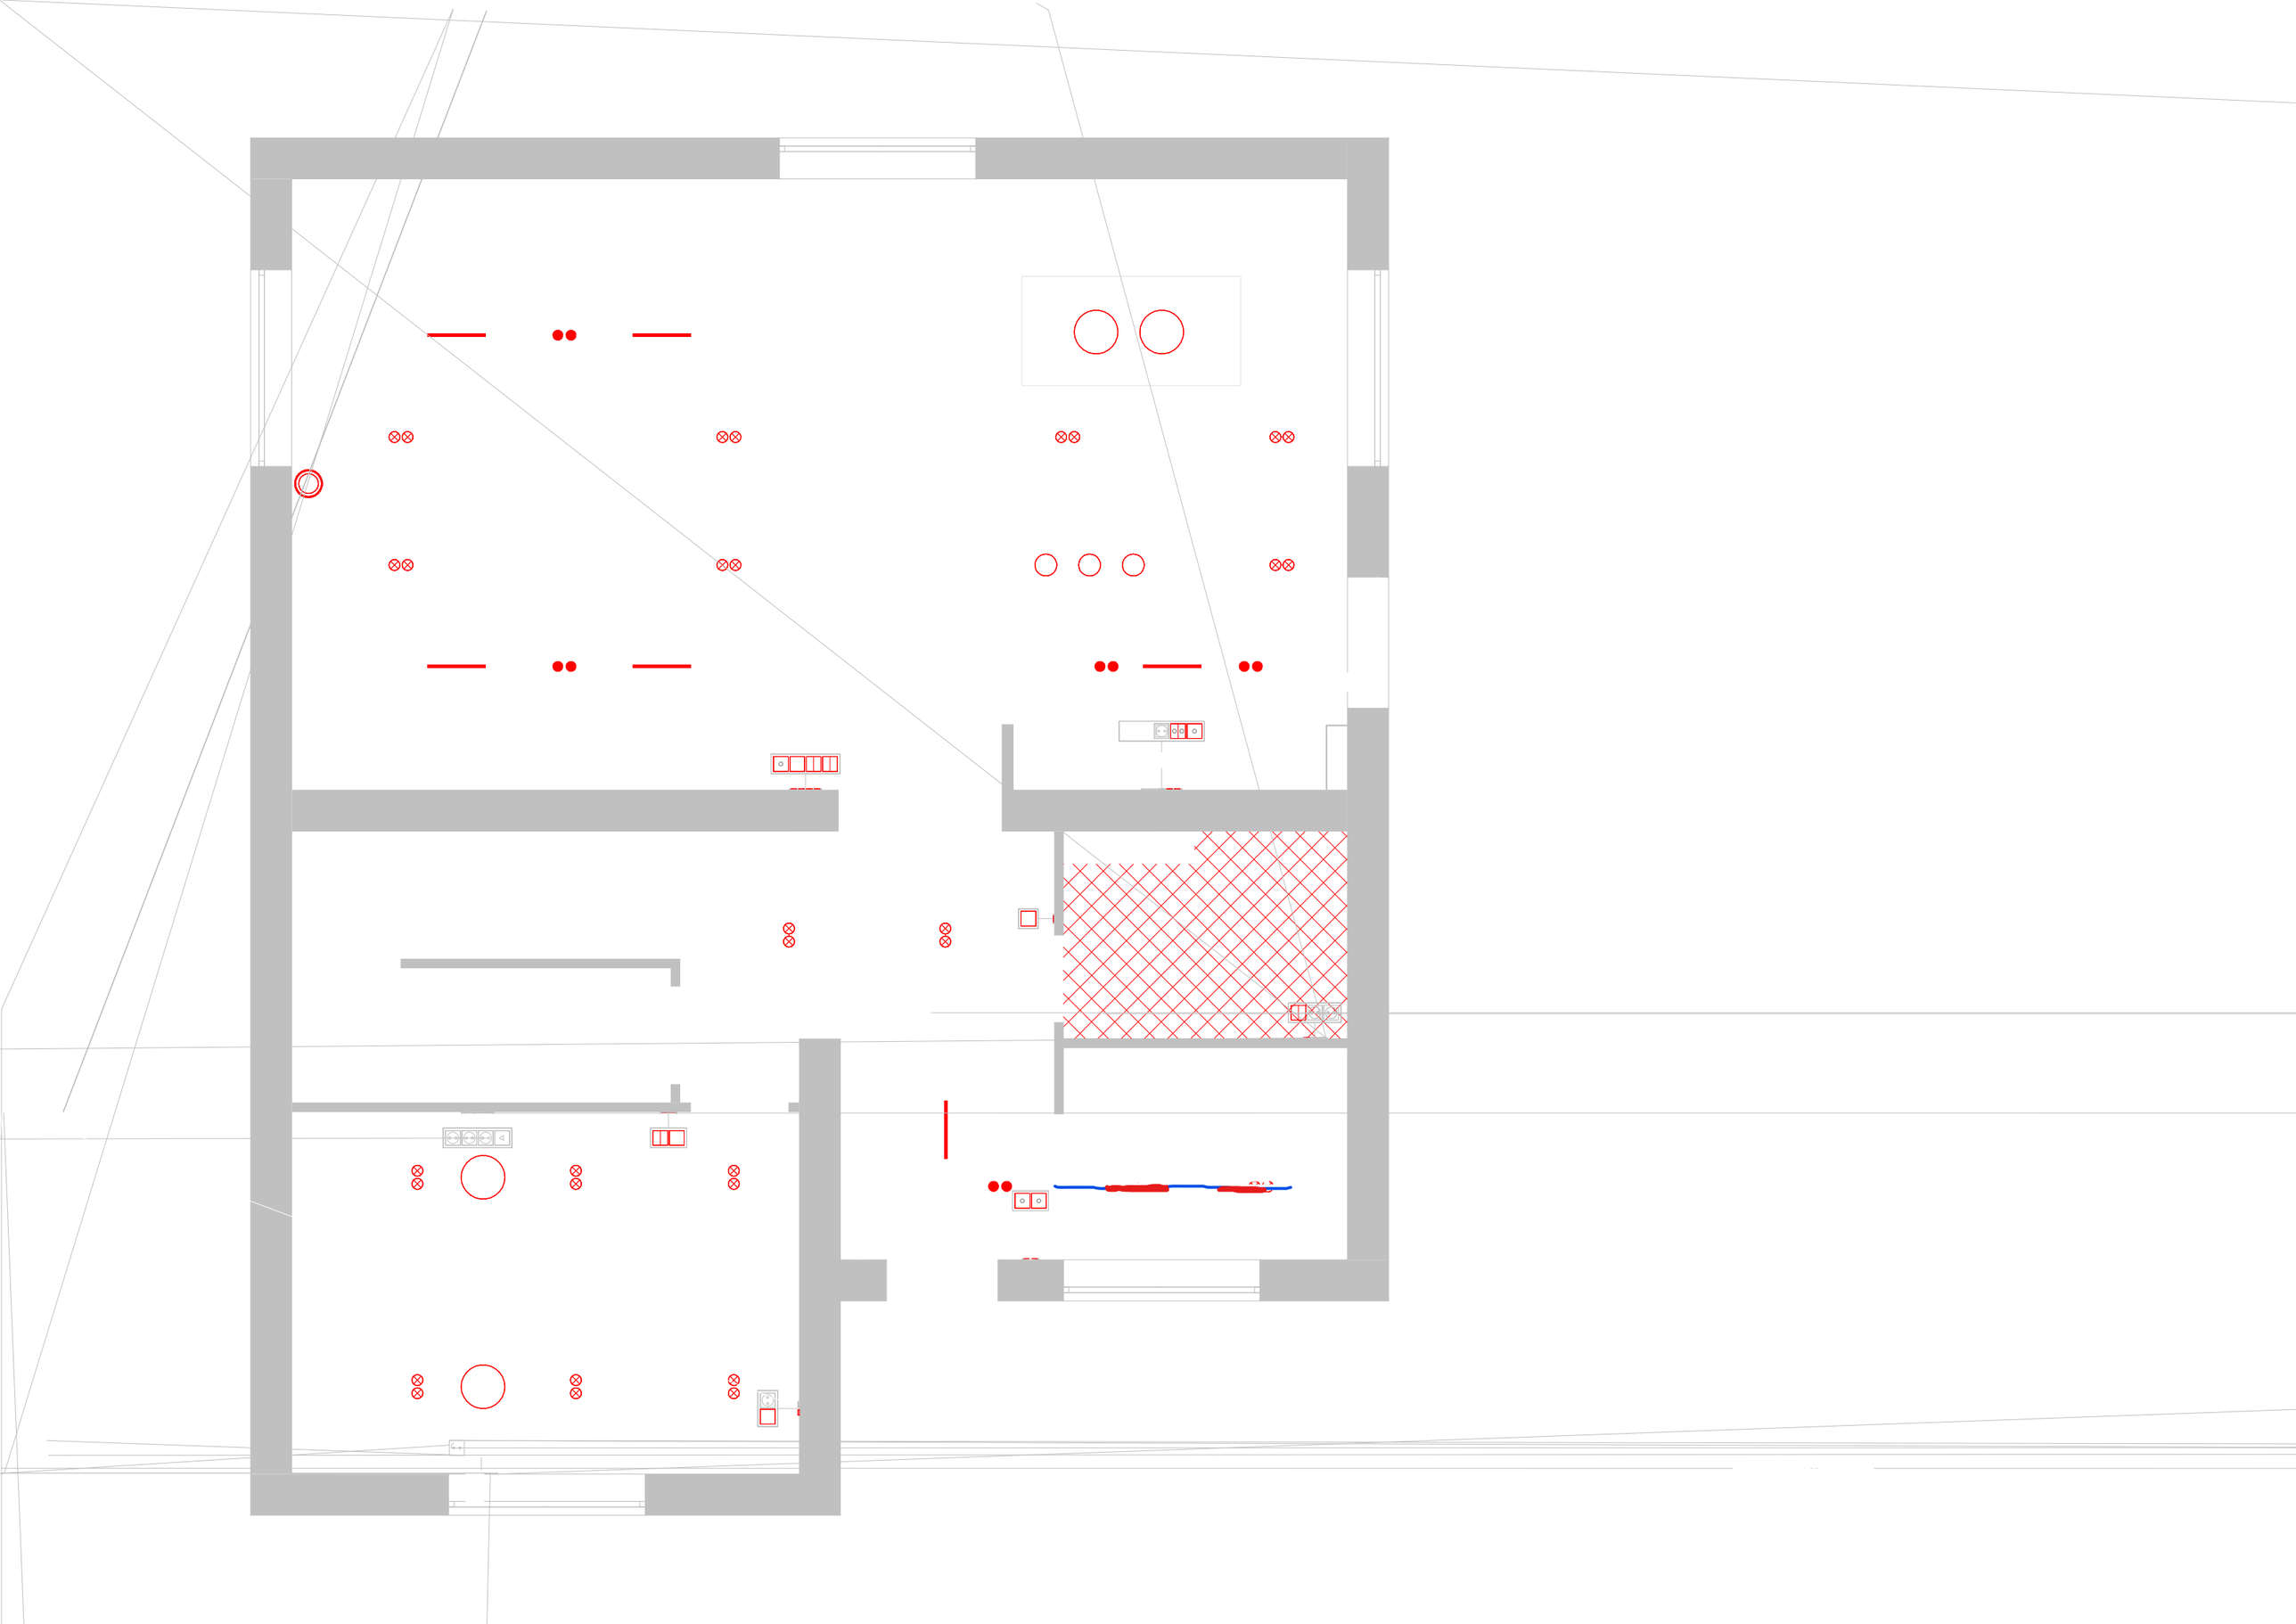

 

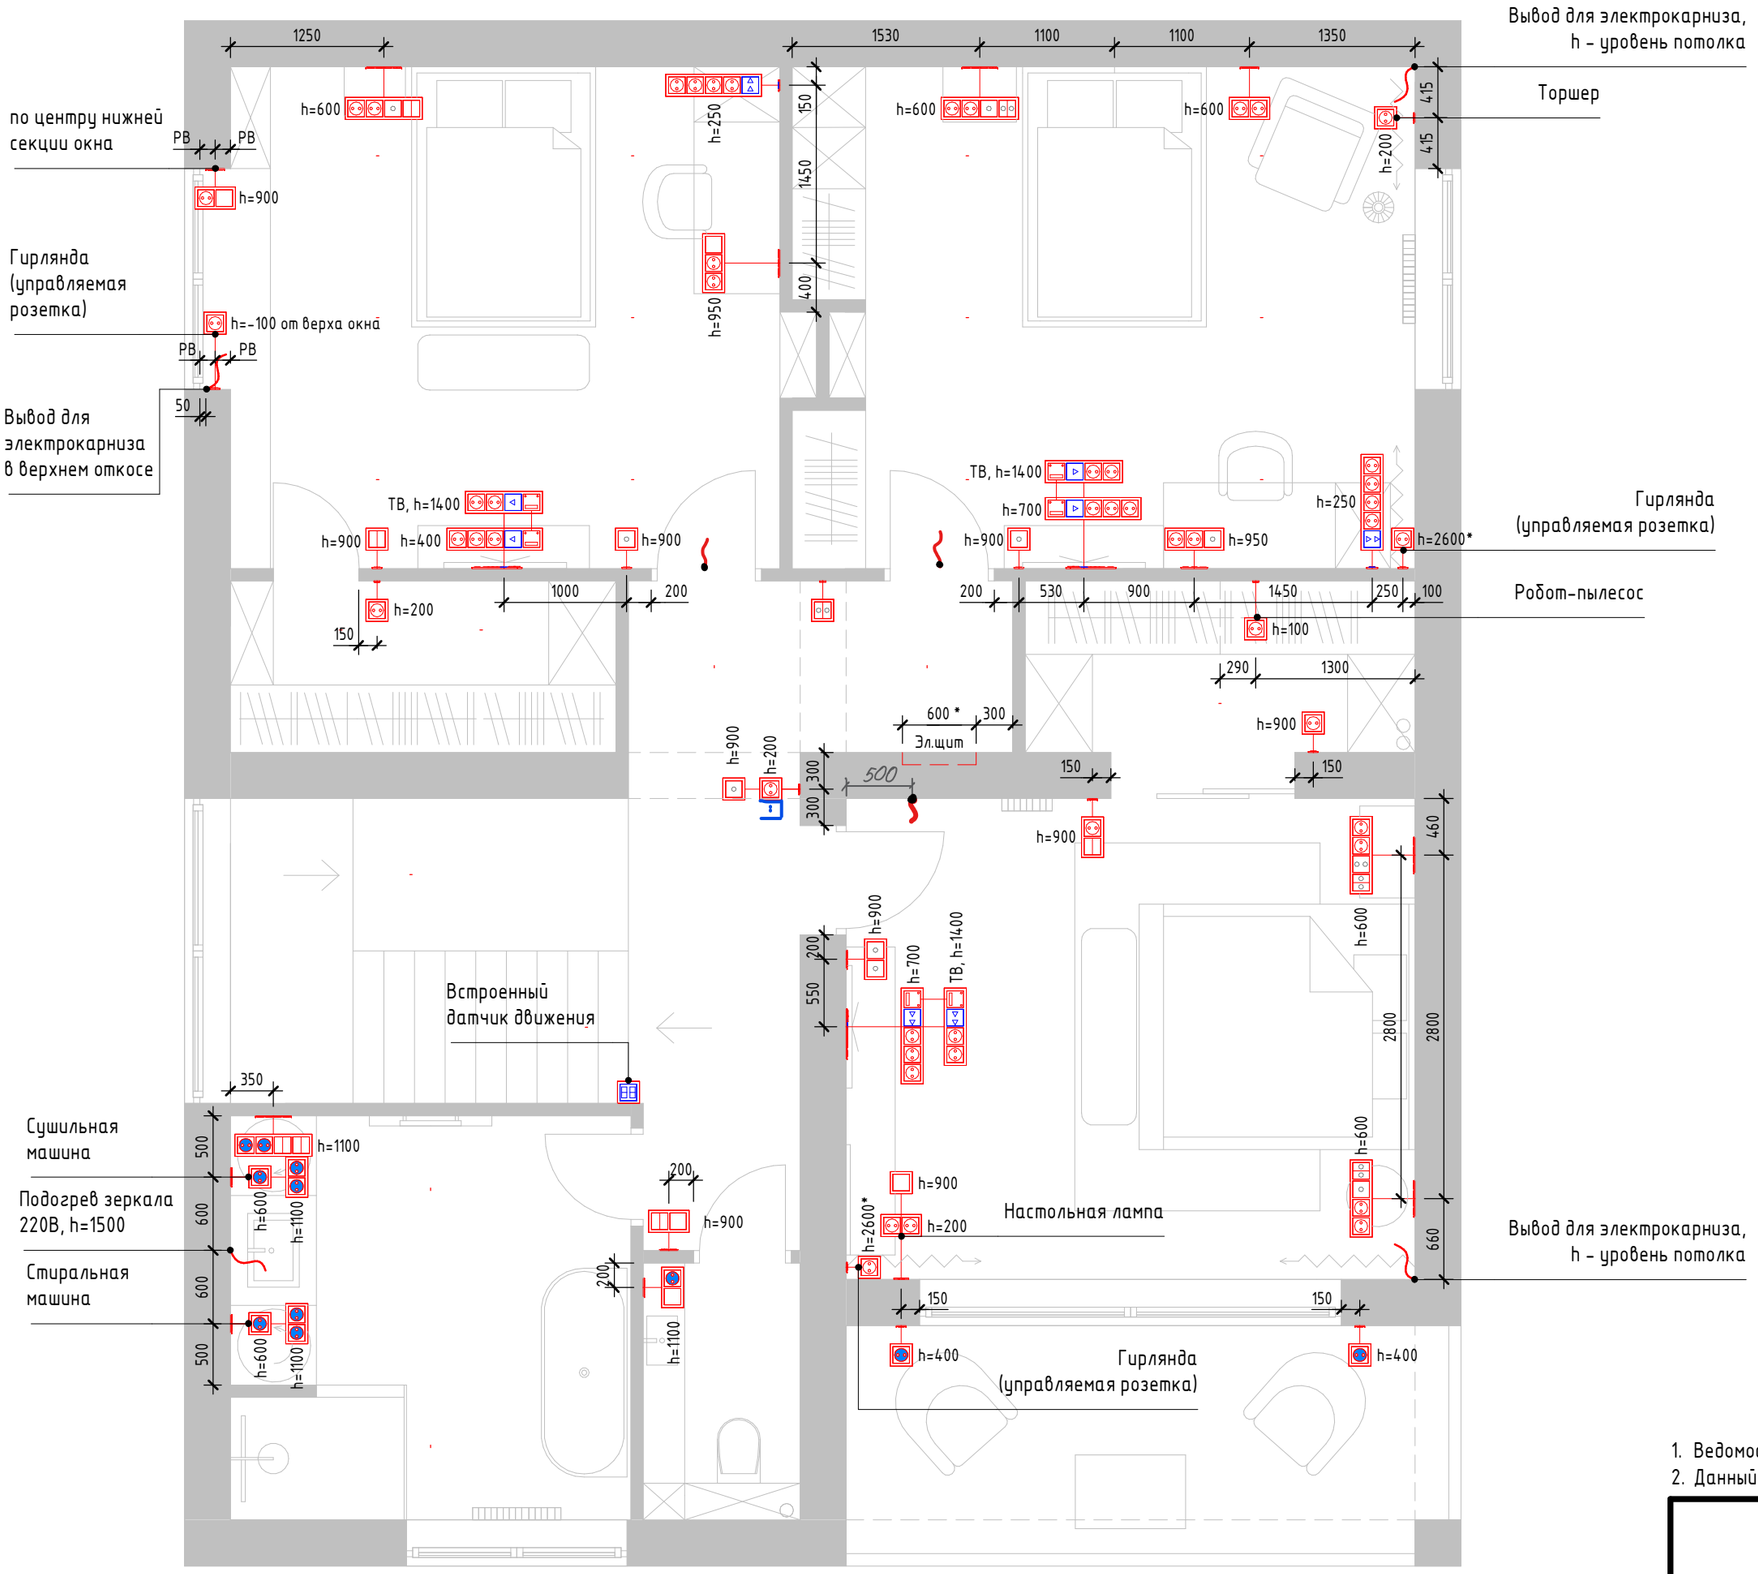

Условные обозначения электрофурнитуры:

- Выключатель одноклавишный
- Выключатель двухклавишный
- Выключатель одноклавишный (мастер)
- Переключатель одноклавишный
- Перекрестный переключатель одноклавишный
- Переключатель двухклавишный
- Видеодомофон
- eBUS Панель управления отоплением
- POE Панель управления умным домом
- Заглушка кабель-канала
- Розетка 220В
- Розетка 220V IP20 с крышкой
- Розетка 220В IP44
- Мебельный инфракрасный выключатель
- Интернет розетка RJ45 1x
- Интернет розетка RJ45 2x
- Датчик движения и освещения

1. Ведомость электрофурнитуры и примечания см.л. 2
2. Данный лист читать совместно с листами 2, 4, 6

	Стадия	Лист	Листов
	П	05	
План электрики. Второй этаж	*Елена Рыдикова* *+7 927 287 88 49*		

Формат А3А

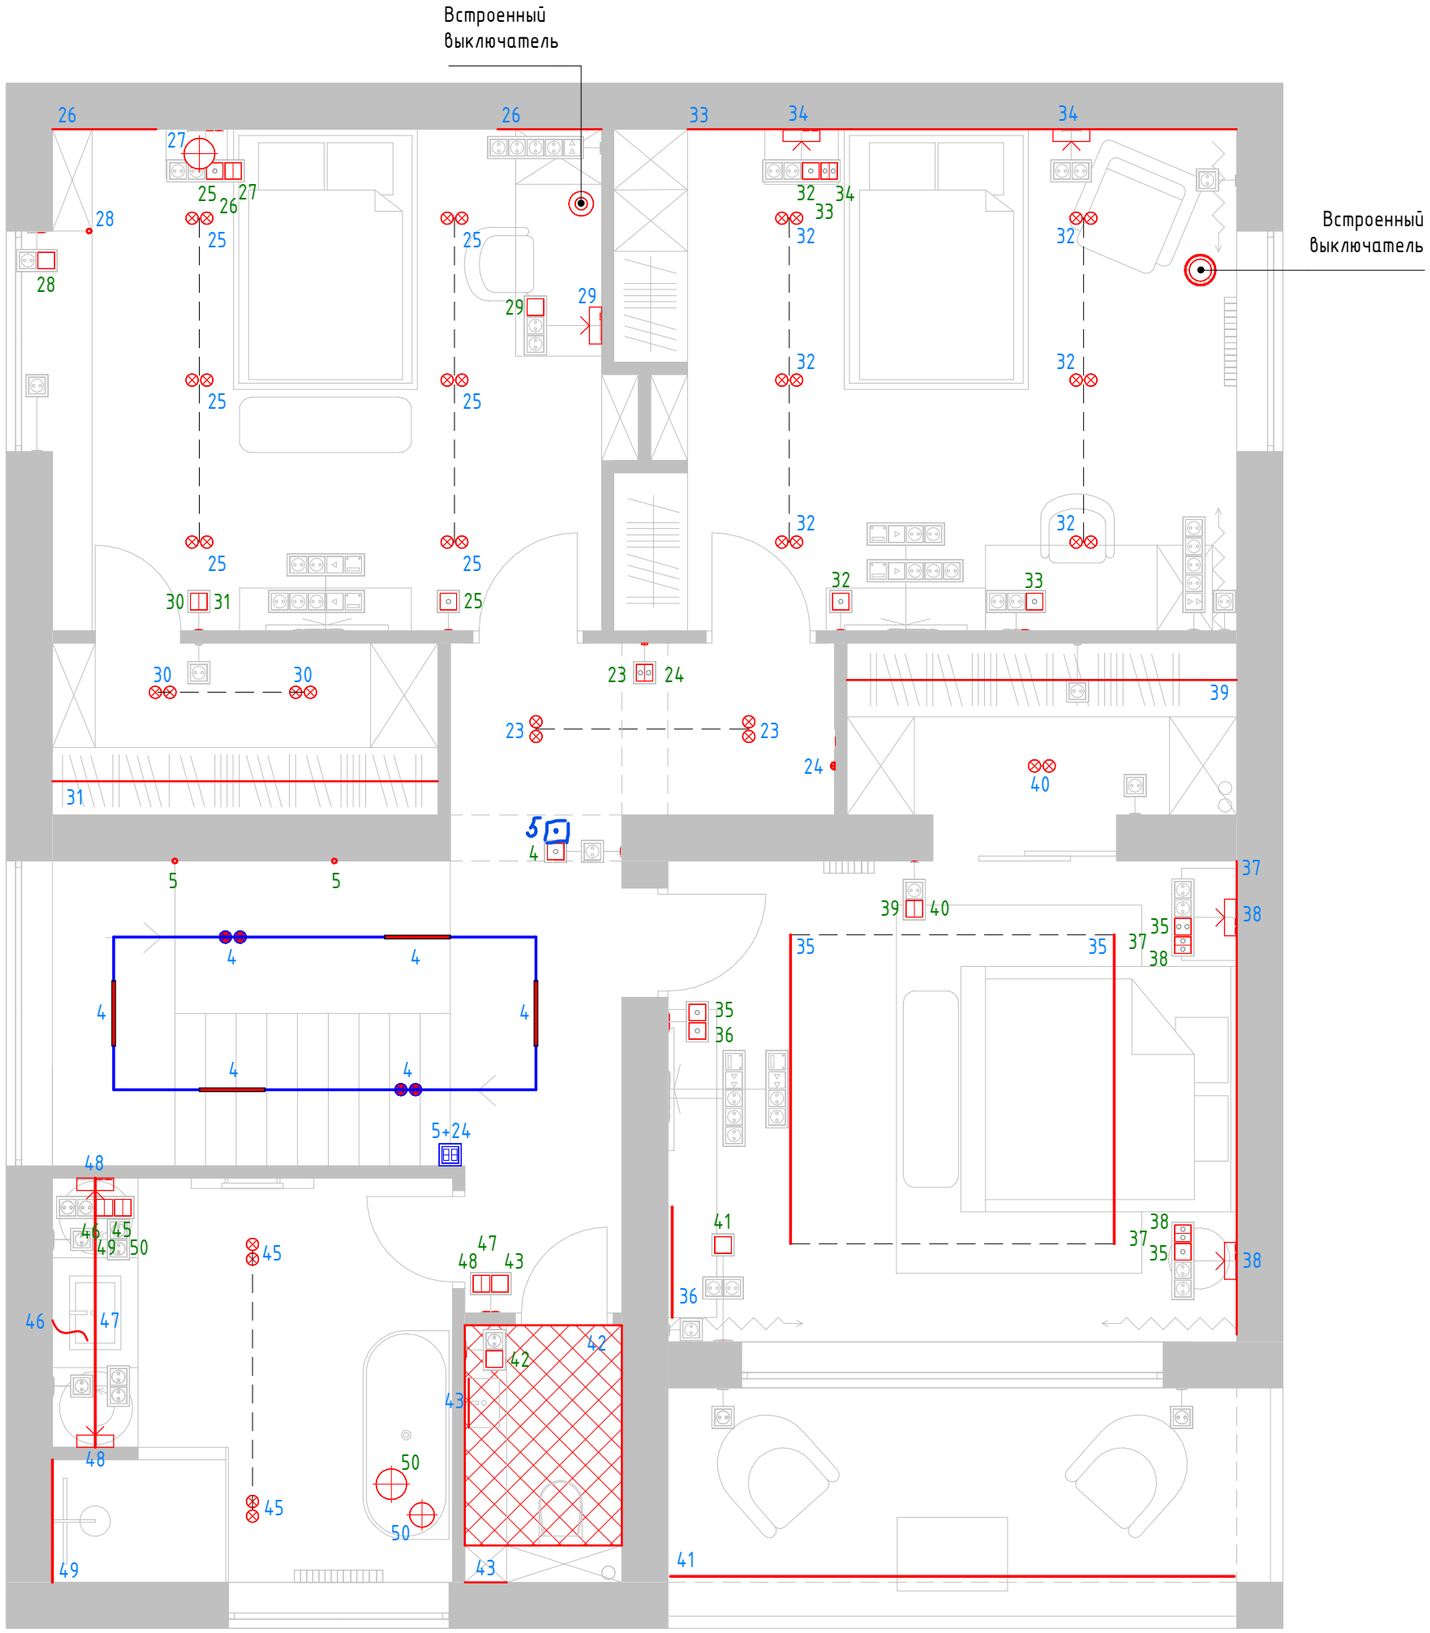

Условные обозначения электрофурнитуры:

- Выключатель одноклавишный
- Выключатель двухклавишный
- Выключатель одноклавишный (мастер)
- Переключатель одноклавишный
- Перекрестный переключатель одноклавишный
- Переключатель двухклавишный
- Видеодомофон
- eBUS Панель управления отоплением
- POE Панель управления умным домом
- Заглушка кабель-канала
- Розетка 220В
- Розетка 220V IP20 с крышкой
- Розетка 220В IP44
- Мебельный инфракрасный выключатель
- Интернет розетка RJ45 1x
- Интернет розетка RJ45 2x
- Датчик движения и освещения

1 · Точка ввода

1 · Точка вывода

1 · Включение вытяжного вентилятора

1. Данный лист читать совместно с листами 1, 2

	Стадия	Лист	Листов
	П	06	
Схема групп включения. Второй этаж	*Елена Рыдикова* *+7 927 287 88 49*		

Формат А3А